

ARCHITECTURE ISLAMIQUE

Chapitre II PARTIE 2

- Période 1: De 610 à 661
- Période 2 : De 661 à 750
- Période 3: De 750 à 945

- Spécificités spatiales et structurelles
- Etymologie
- Typologies spatiales

3. Typologie des bâtiments

Les fonctions d'un bâtiment peuvent être multiples (mosquée et madrasa, par exemple). Il arrive souvent que des archéologues ne soient pas en mesure d'identifier exactement le bâtiment auquel ils ont à faire car des plans identiques peuvent être utilisés pour différents types d'édifices.

1. La mosquée

La mosquée est le lieu de prière pour les musulmans. L'édifice sert à rassembler la communauté musulmane

En arabe, *mosquée* se dit « *masjid* », du mot *sajada*, se prosterner.

Types de mosquées :

- La *mosquée de quartier*
- La *mosquée du vendredi*, dite aussi *mosquée congrégationnelle* ou *Grande mosquée*. Comme son nom l'indique, elle sert principalement pour la grande prière du vendredi,
- La Musalla: est un lieu de prière en plein air, généralement situé en dehors des villes, qui sert lors des grandes fêtes religieuses.

Éléments constitutants d'une mosquée :

1. **L'enceinte** : sépare la mosquée du monde extérieur.
2. **La salle de prière ou Haram** : c'est le lieu de la prière. Le sol est toujours recouvert de tapis afin de le purifier.
3. **La fontaine** : indispensable dans une mosquée pour faire les ablutions rituelles.
4. **Le minaret** : grande tour, d'où le muezzin lance l'appel à la prière. Le minaret sert surtout à marquer l'emplacement d'un sanctuaire, car on le voit de loin. Sa forme varie selon les régions et les époques.
5. **Le mihrab** : élément le plus important du bâtiment, car il indique la Qibla. Il a en général la forme d'une niche plus ou moins profonde et plus ou moins grande.
6. **Le minbar** : chaire à prêcher. En bois ou en tout autre matériau (pierre, marbre par exemple), il se situe toujours juste à côté du mihrab.
7. **La dikka** : On n'en trouve que dans les grandes mosquées. C'est la tribune qui permet de répercuter dans la salle de prière le sermon du muezzin.
8. **La Maqsura** : c'est l'endroit clos situé près du mihrab, réservé au souverain pour le protéger des attaques. Elle n'est pas présente dans toutes les mosquées.

Les différents plans de mosquées :

1. Plan arabe


C'est le premier plan conçu. Il se base sur un modèle plus ou moins mythique : la maison du Prophète à Médine.

Le plan arabe, ou **plan hypostyle***, se compose d'une cour à portique et d'une salle de prière à colonnes,

les **nefs** étant dirigées parallèlement ou perpendiculairement (pour le Maghreb et certaines exceptions) à la qibla. On le trouve dans tout le monde islamique, depuis la Syrie (**Grande mosquée de Damas**, par exemple) jusqu'au Maghreb (exemple la **Grande mosquée de Kairouan**, dont l'aspect actuel remonte au IX^e siècle), à l'Espagne et à l'Irak.

* Une **salle hypostyle** est un espace fermé dont le plafond est soutenu par des colonnes.

UNE MOSQUÉE

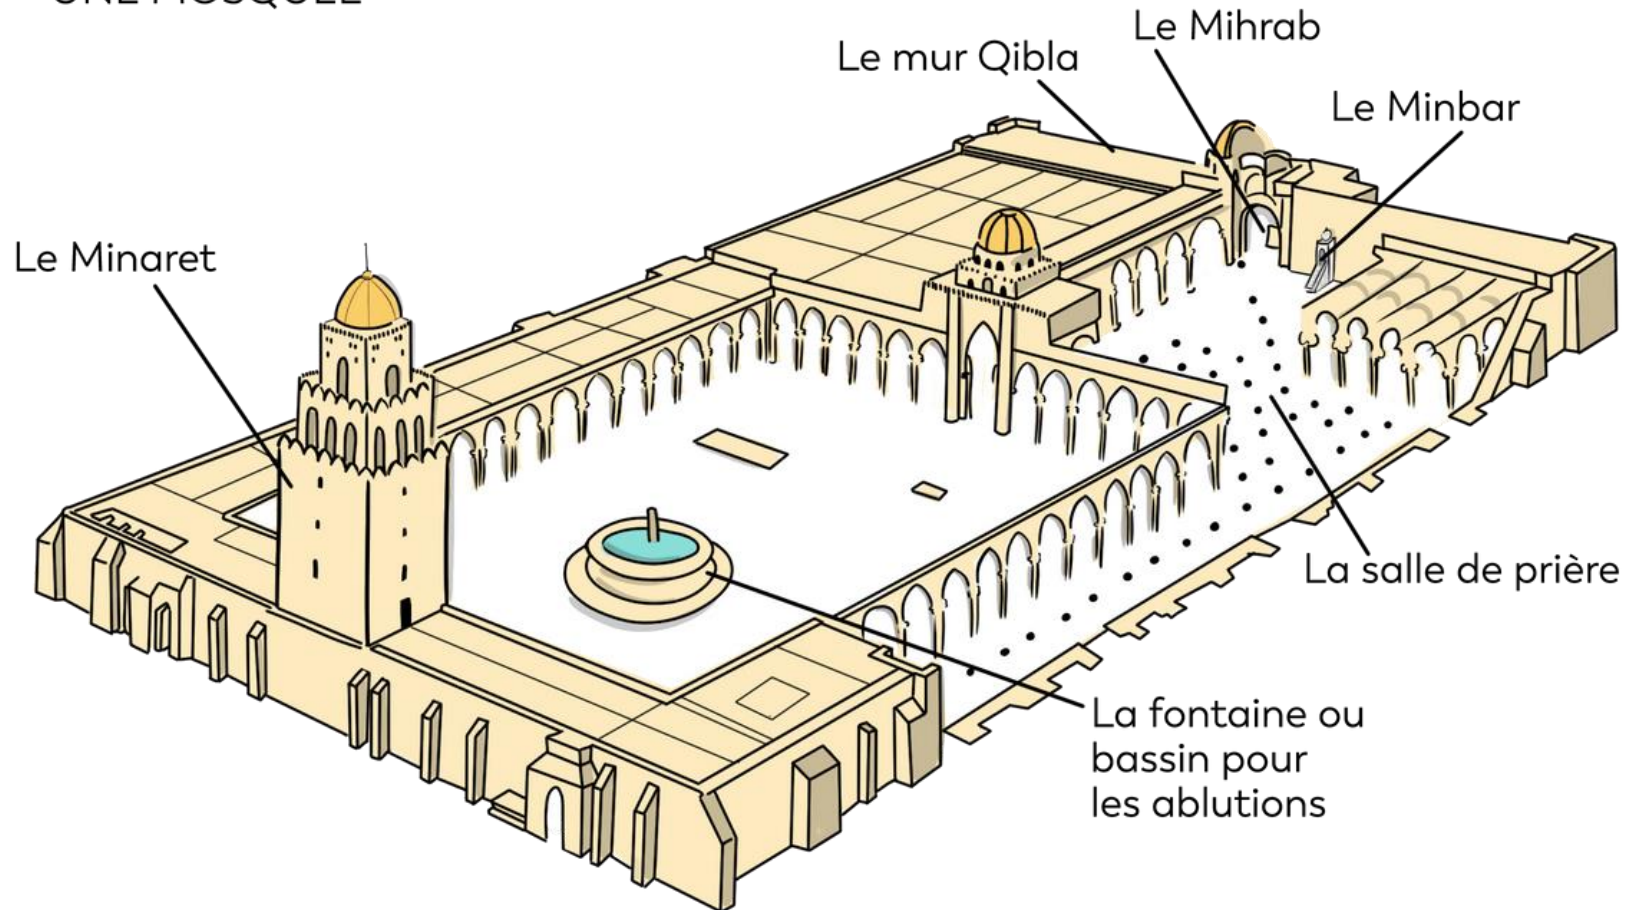


Kairouan, la Grande Mosquée de Sidi Uqba

Ensemble et plan de la Grande Mosquée de Sidi Uqba, à Kairouan (Tunisie). VIIIe-Xe siècle.

HCA Première année Archi. Archi islamique Chapitre 2 Partie 2.


Mme Boudinar. 2023-2024

Vues tridimensionnelles de la Grande Mosquée de Kairouan

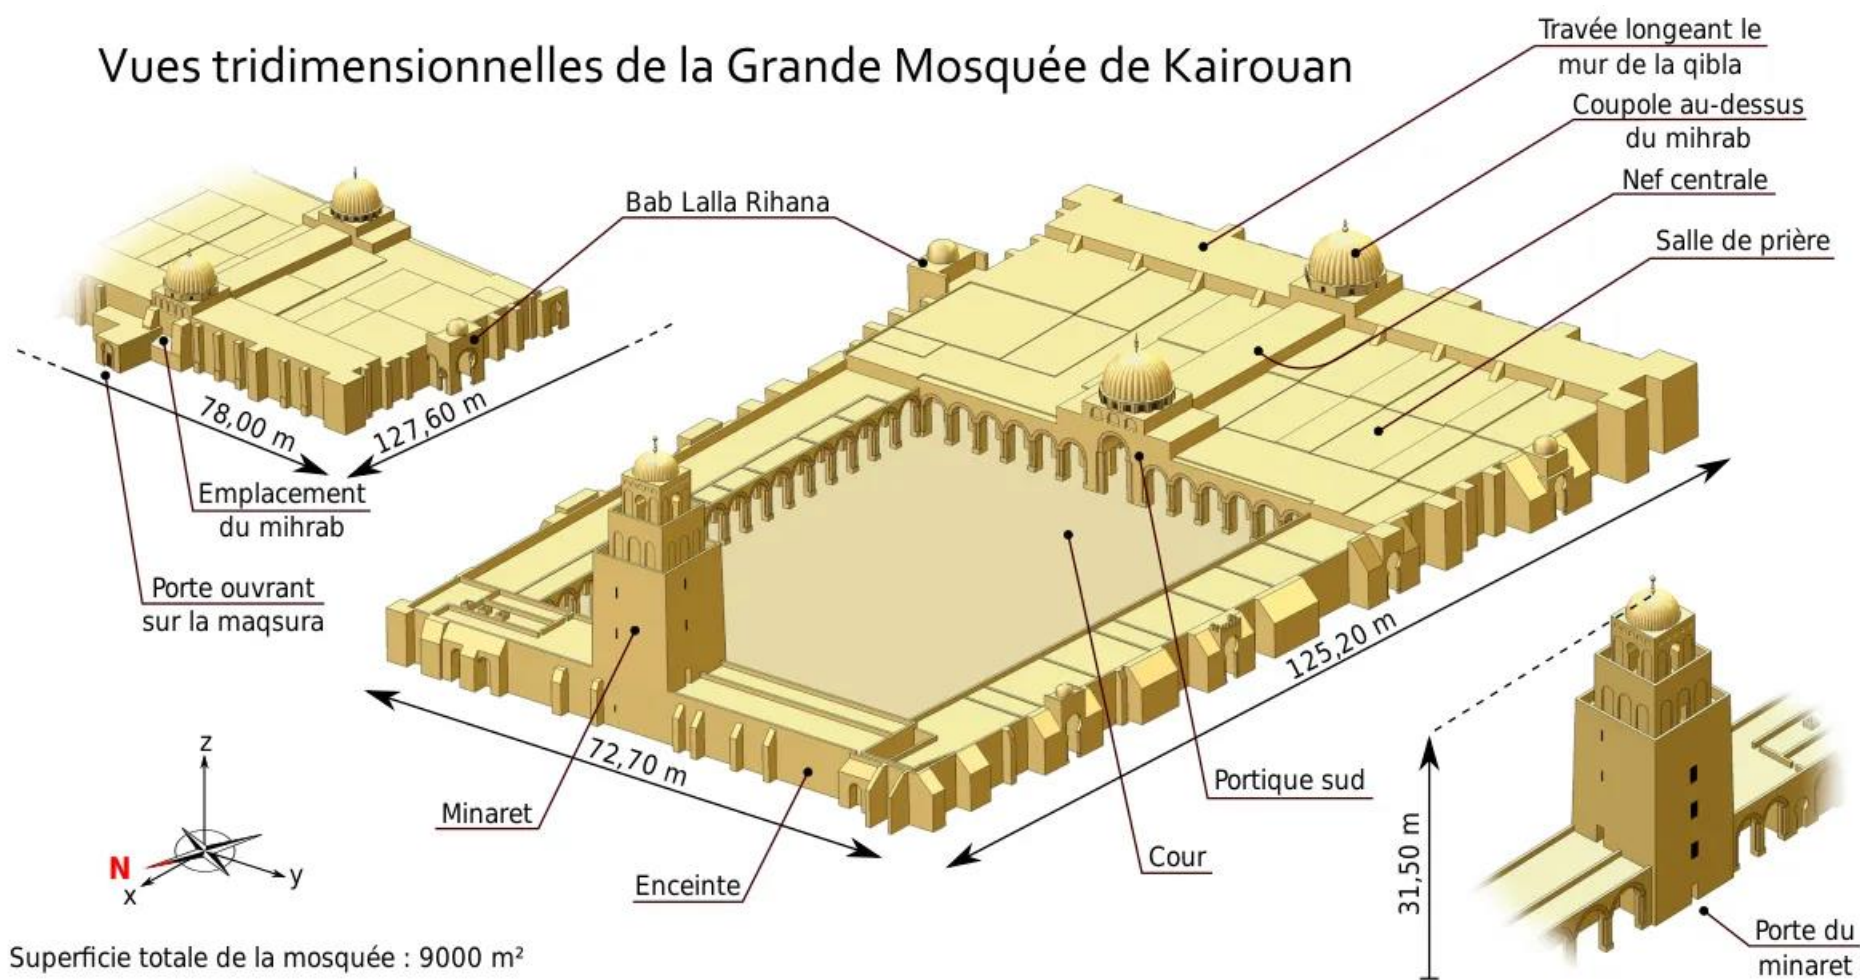

LA MOSQUEE DE KAIROUAN Tunisie

Plan

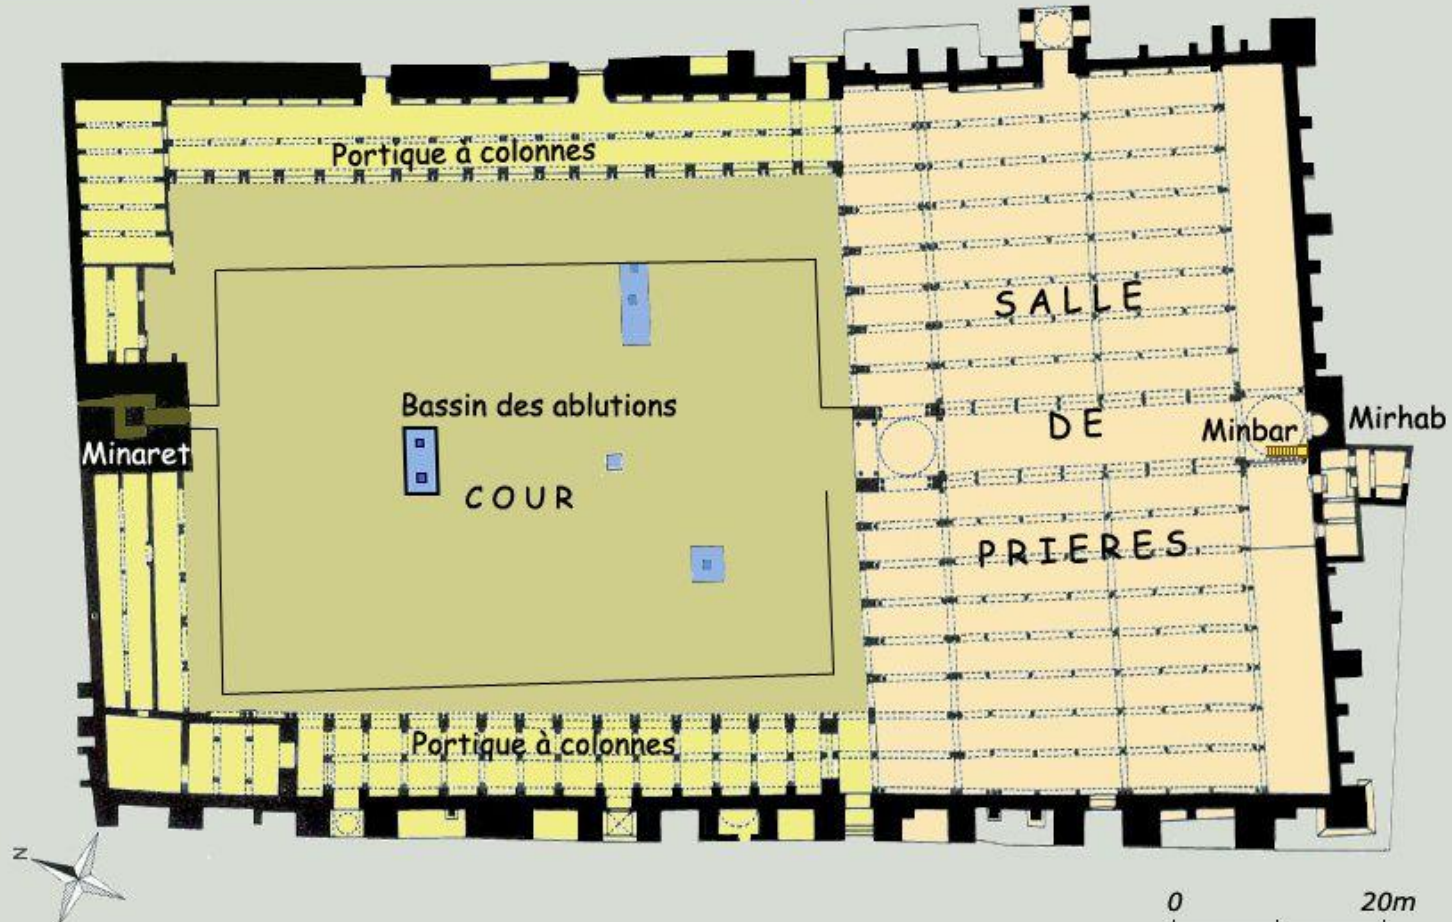

Kairouan, la Grande Mosquée de Sidi Uqba

Ensemble et plan de la Grande Mosquée de Sidi Uqba, à Kairouan (Tunisie). VIIIe-Xe siècle.

HCA Première année Archi. Archi islamique Chapitre 2

Partie 2. Mme Boudinar. 2023-2024

2. Plan Perse

Ce plan se retrouve dans la région de l'Iran (partiellement l'Afghanistan, le Pakistan et l'Irak). Mais aussi en Inde avant la dynastie moghole et dans l'actuel territoire de l'Ouzbékistan .


Il apparaît au **X^e siècle** avec la dynastie **Seldjoukide** et se caractérise par l'emploi d'**iwans**, d'un **pishtak** et **une salle de prière sous coupole**.

La **mosquée du Shah** construite par le souverain safavide Shah Abbas Ier entre 1612 et 1630 est l'un des plus beaux exemples de plan iraniens connus.

Rappel:

Un iwan est une salle voûtée ouverte sur un côté par un grand arc inclus dans une encadrement rectangulaire

Un pishtak est un portail formant une avancée, souvent surmonté de deux minarets et ouvert par un grand arc.

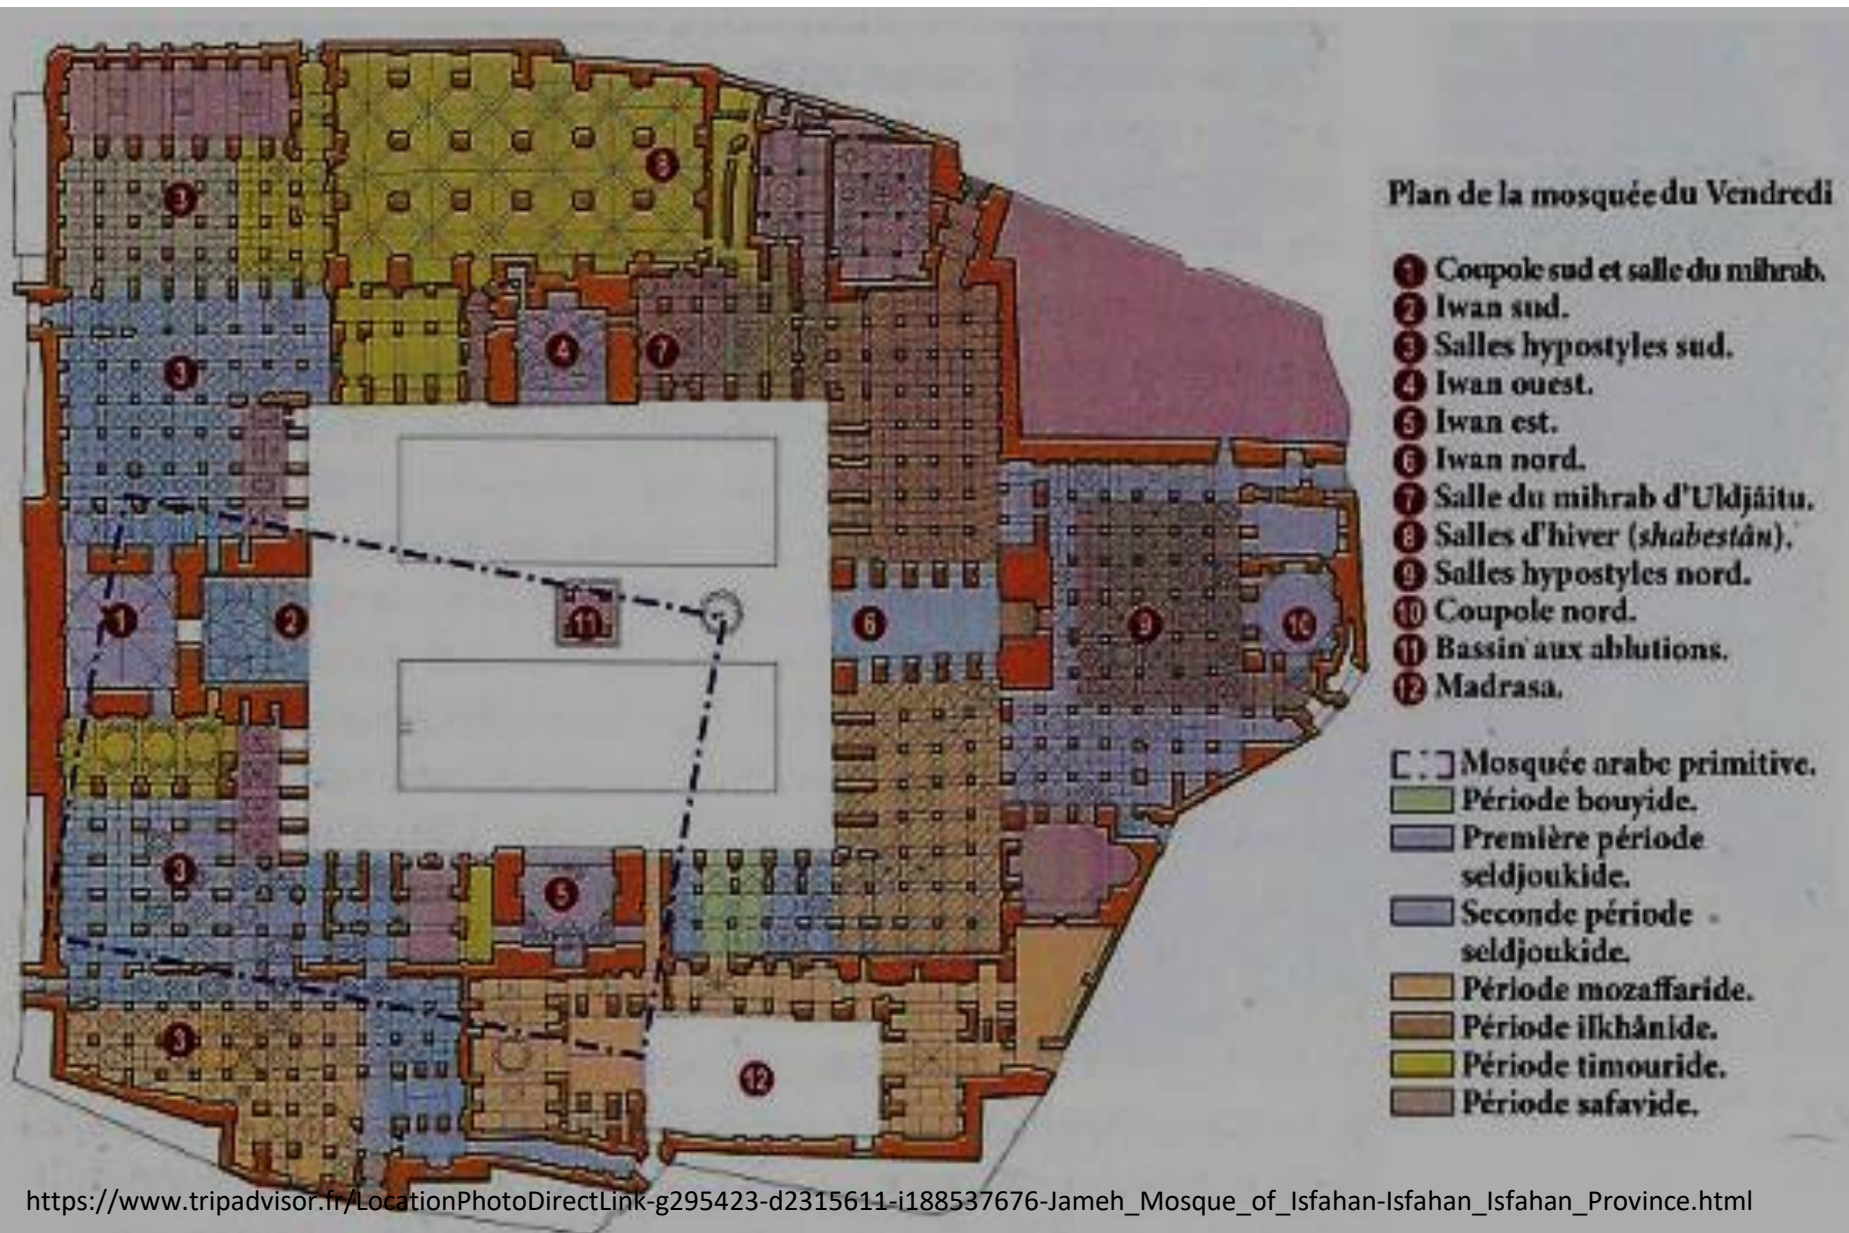

C'est lors de sa reconstruction au XIIe s. qu'est adopté le plan persan avec une cour à quatre iwans. L'iwan Sud est le plus remarquable avec ses deux minarets, ses muqarnas monumentaux et leurs inscriptions en écriture koufique. Son décor de céramiques est splendide.



Dans les salles hypostyles qui l'encadrent le décor est en briques disposées de multiples manières sur les colonnes et les voutes.


A la droite de l'iwan Ouest dans une salle de prière se trouve le bijou de la mosquée le mihrab dit d'Uldjaitu avec sa calligraphie, ses décors végétaux finement sculptés dans le stuc, une merveille qui date de 1210.




le s, sur trompes au beau décor en

de l'architecture et des arts décoratifs de

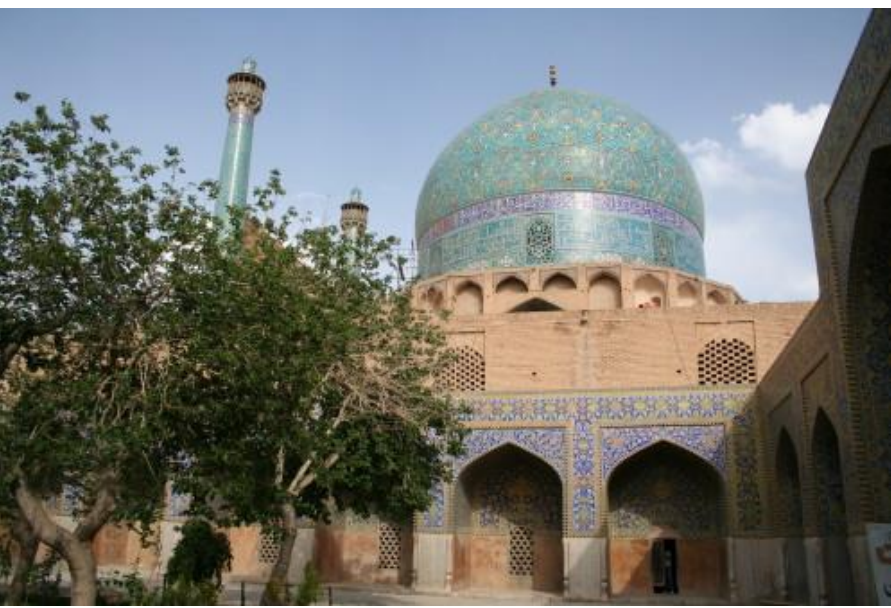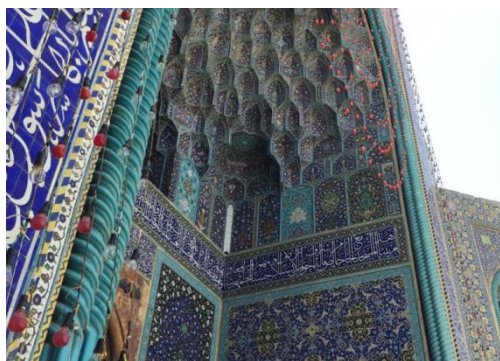

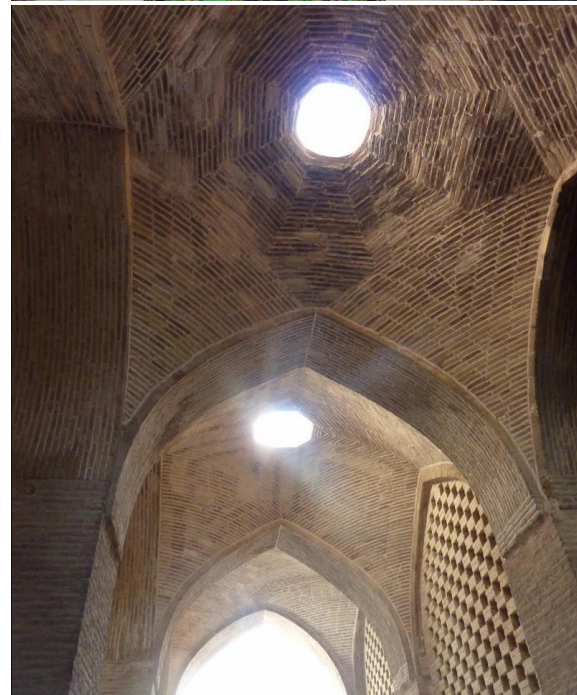


L'art Safavide : peinture et fresque

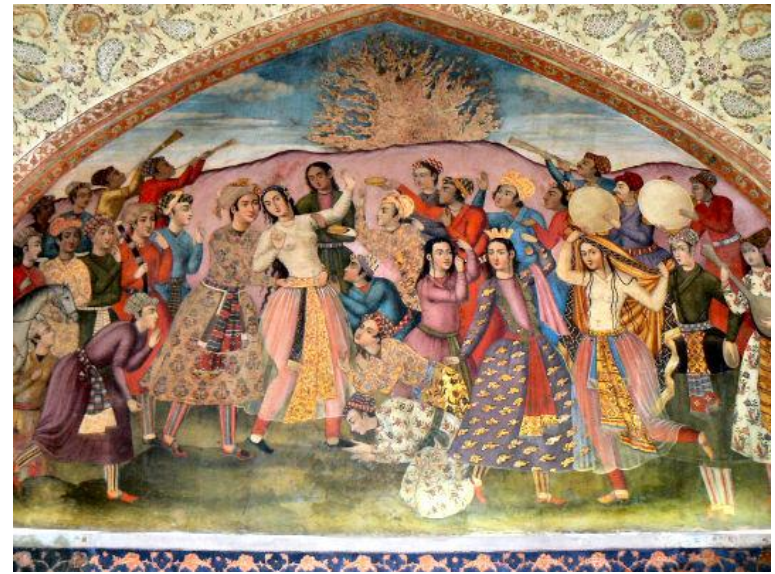

L'architecture de la mosquée persane miniaturise ainsi un ordre à la fois transcendant et universel : sa cour est un miroir du monde, ses coupoles sont des cieux, les émaux du décor sont les couleurs « cristallines » d'un monde immatériel et surnaturel, les ornements végétaux matérialisent les jardins édéniques du Coran, l'ombre des iwans préfigure la fraîcheur du paradis, le bleu des décors reflète le Ciel, le bassin est la source de Vie ou le miroir spirituel du cœur.

Les croyants rassemblés entre ses murs et sous ses coupoles prient dans **un espace qui se veut une synthèse de l'univers émané de Dieu et un souvenir du paradis et de ses jardins.**

Le mihrab dit d'Uldjâitu fut créé en 1310. Sculpté dans le plâtre, autrefois peint, il est l'un des plus beaux mihrabs de ce type, d'une virtuosité technique et d'un raffinement esthétique remarquable. Il se trouve aujourd'hui dans une salle de la mosquée du Vendredi d'Ispahan, située à côté de l'iwan ouest.

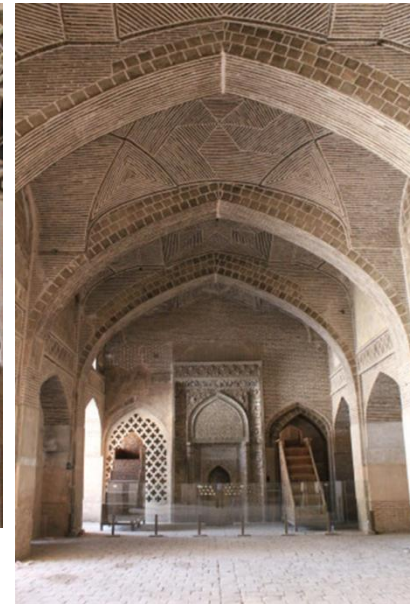

3. Plan Moghol

Ce plan se trouve exclusivement en Inde à partir du **XVI^e s**, et est influencé par le plan Iranien. Il se caractérise par une immense cour à quatre iwans, dont un ouvre sur une salle de prière étroite et rectangulaire, couronnée par trois ou cinq coupoles bulbeuses. Les grandes mosquées de Delhi et de Bîdâr utilisent ce type de plan.




Mosquée de Badshahi, Pakistan, vue de la cour





Mosquée de Jama Masjid. Delhi


Construite par Shah Jahan (de 1644 à 1658), avec ses minarets de 40m. de haut et, au-dessus de la salle de prières, 3 dômes de marbre blanc.

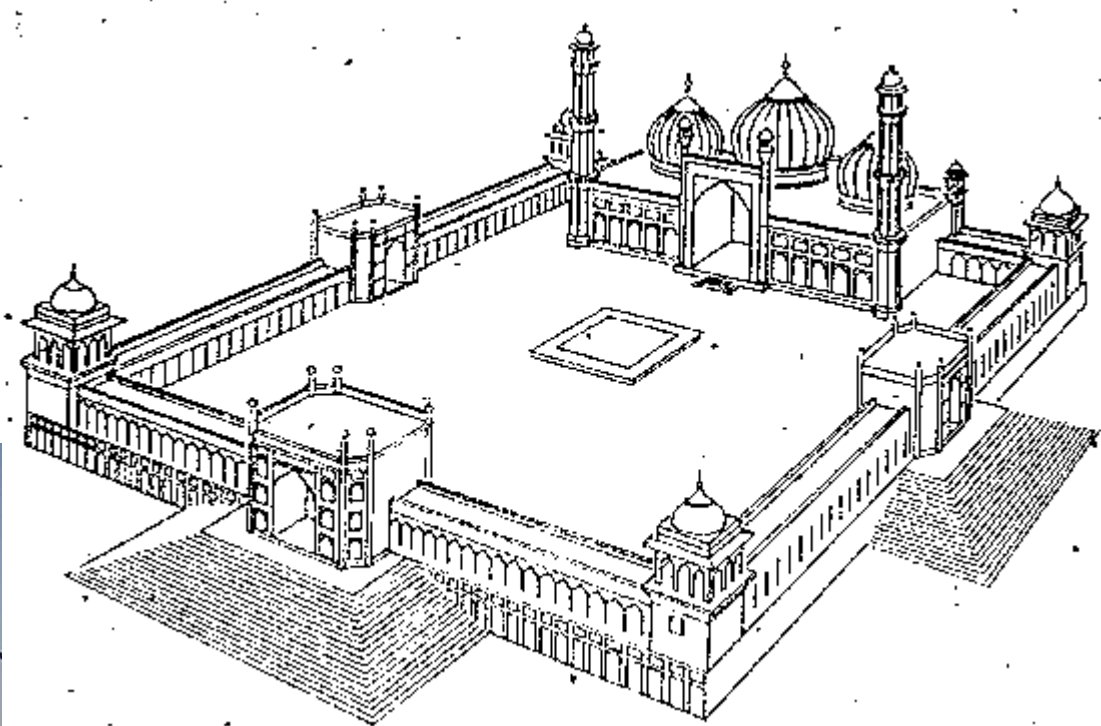


Axonométrie de la grade mosquée. Ensemble palatial de Fatehpur Siri, Inde, 1578

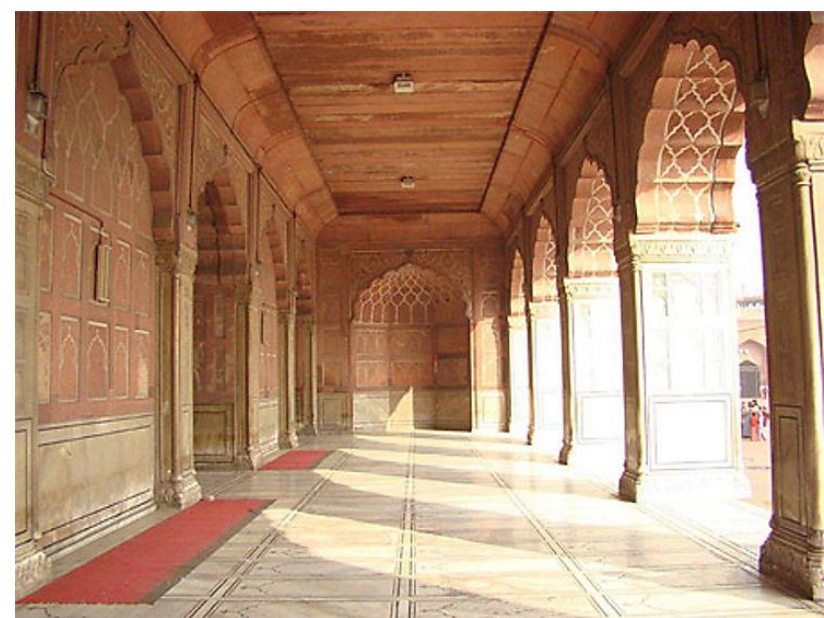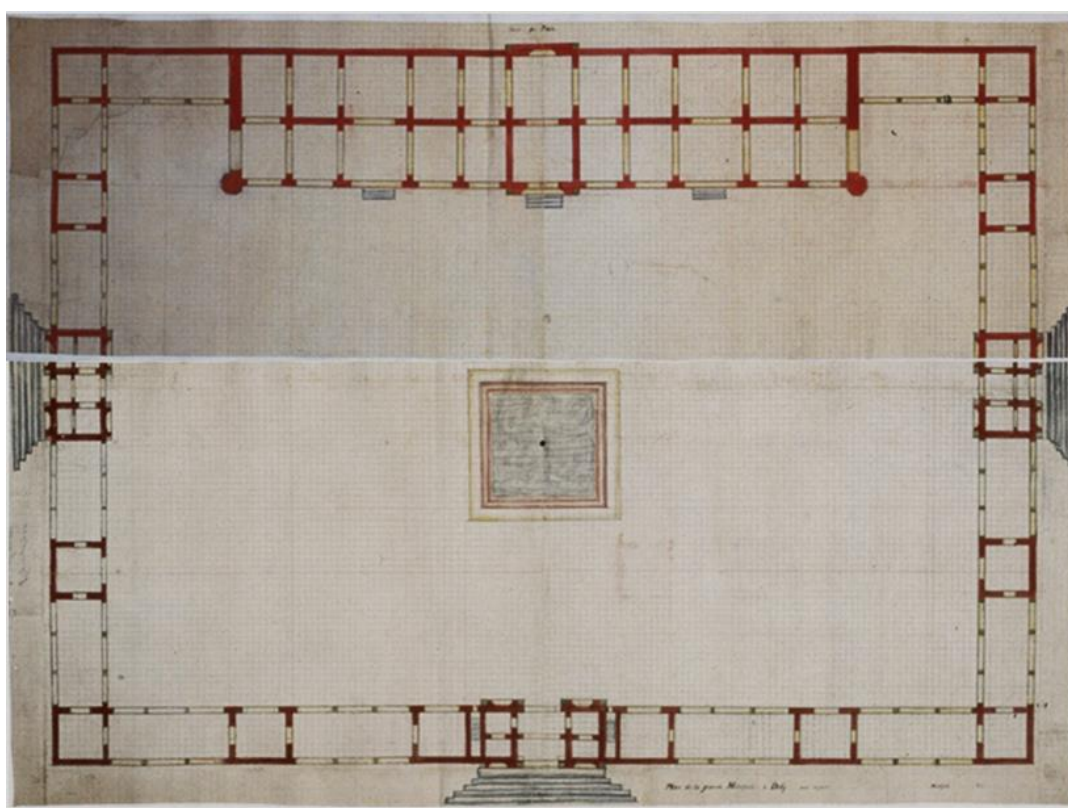

Arcades situées dans la partie antérieure à la Grande Mosquée de Delhi

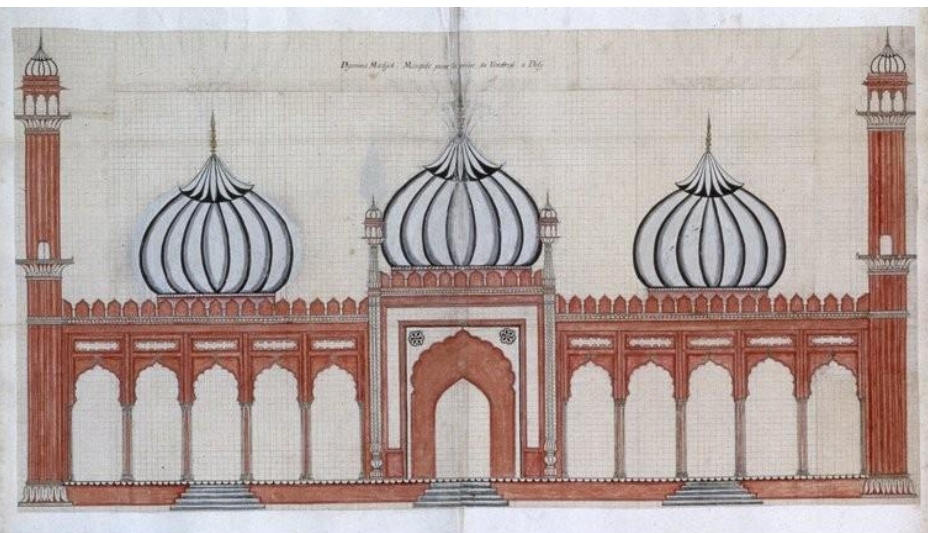

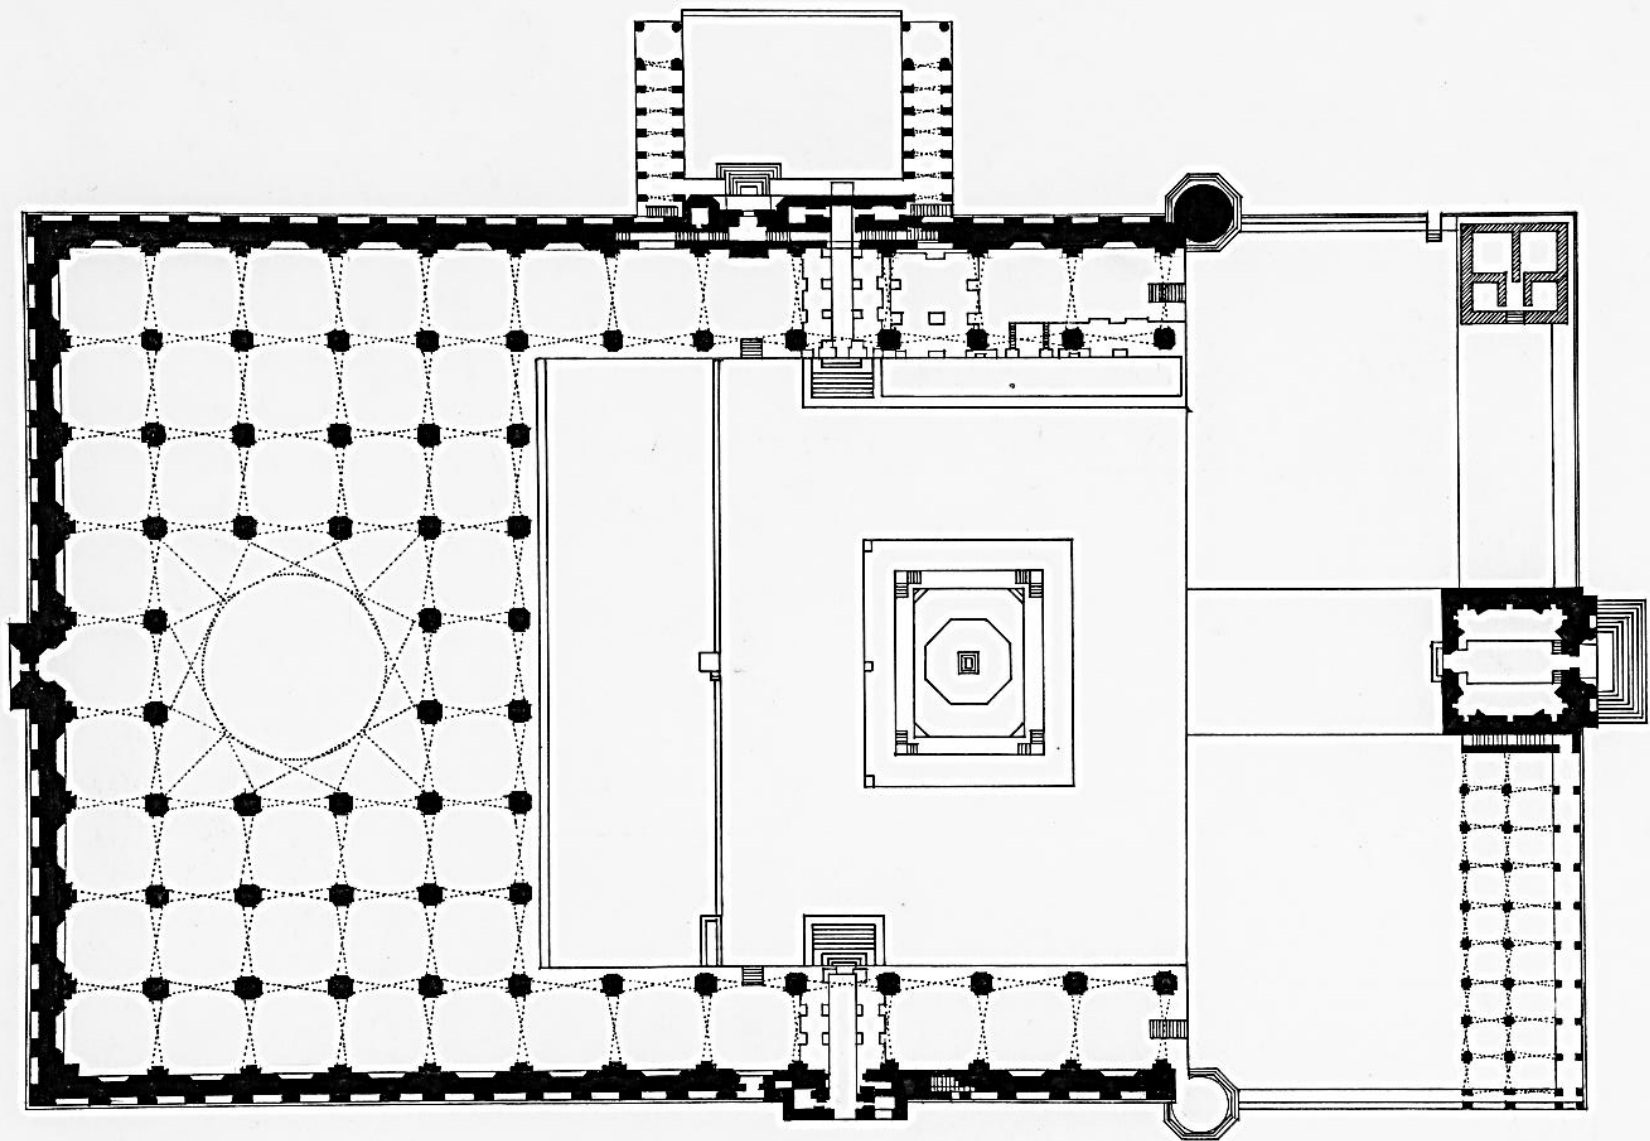


Jamii masjid de Bijapur

HCA Première année Archi. Archi islamique
 Chapitre2 Partie 2. Mme Boudinar. 2023-
 2024

TAJ MOSQUE, AGRA


(SKETCH SHOWING MOSQUE WITH THE NORTHERN CHATRI & THE BAOLI ON THE SOUTH)
SCALE 1/1000

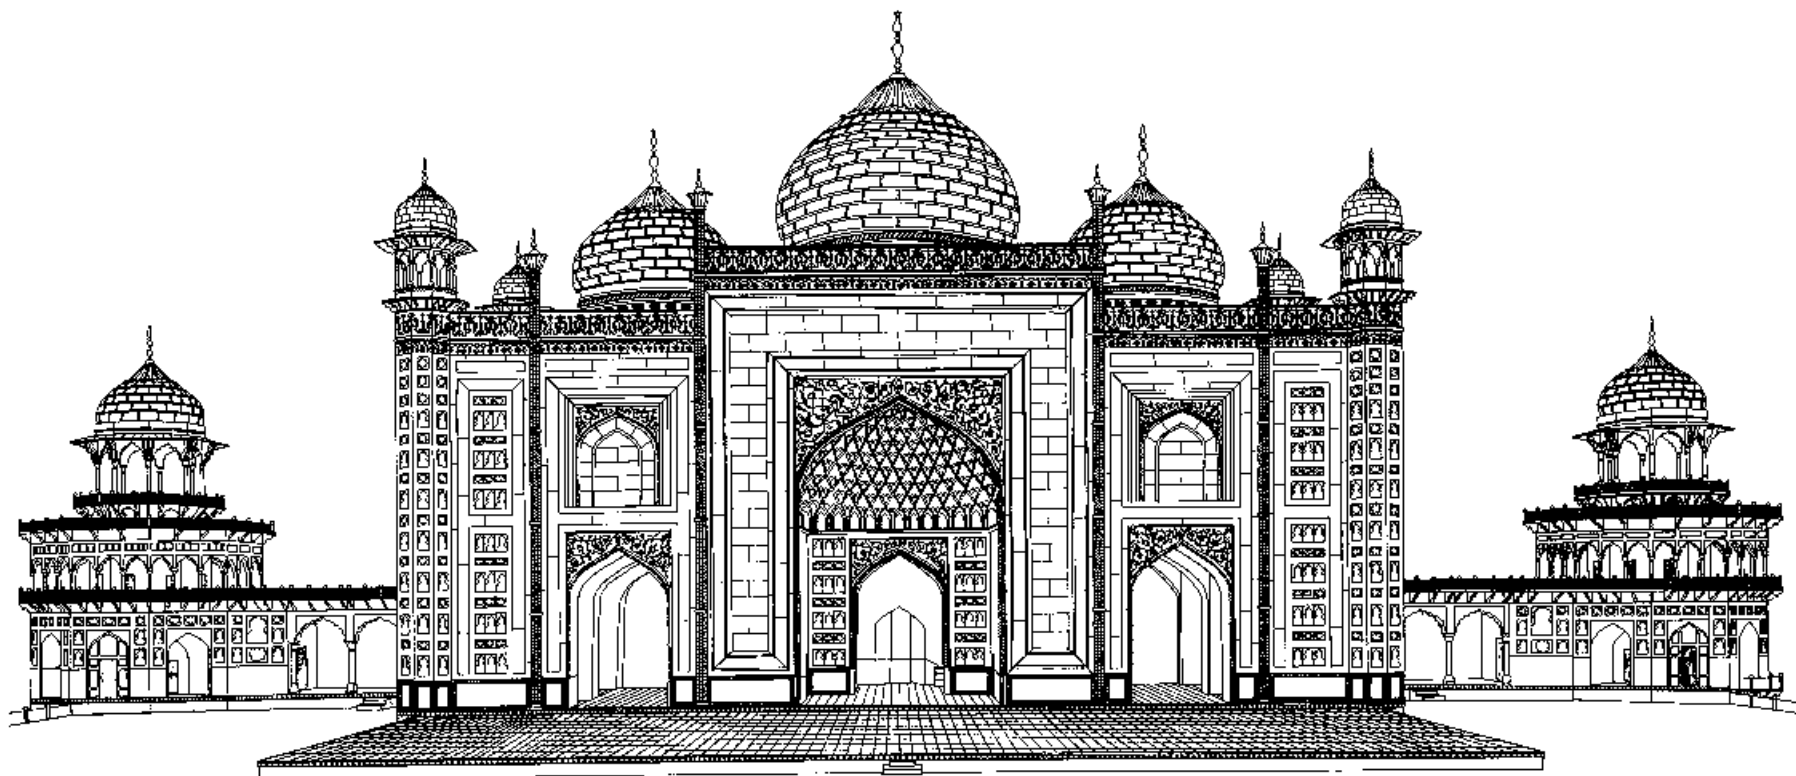

DESIGNED BY: *P. B. Singh*


SKETCHED BY: *H. S. Bhatnagar*
DR. SUPOTTA, ARCHT. ENGINEER

W. H. Bhatnagar
SUPERINTENDING ARCHITECTS,
ARCHAEOLOGICAL SURVEY OF INDIA
NORTH-WEST CIRCLE, AGRA.




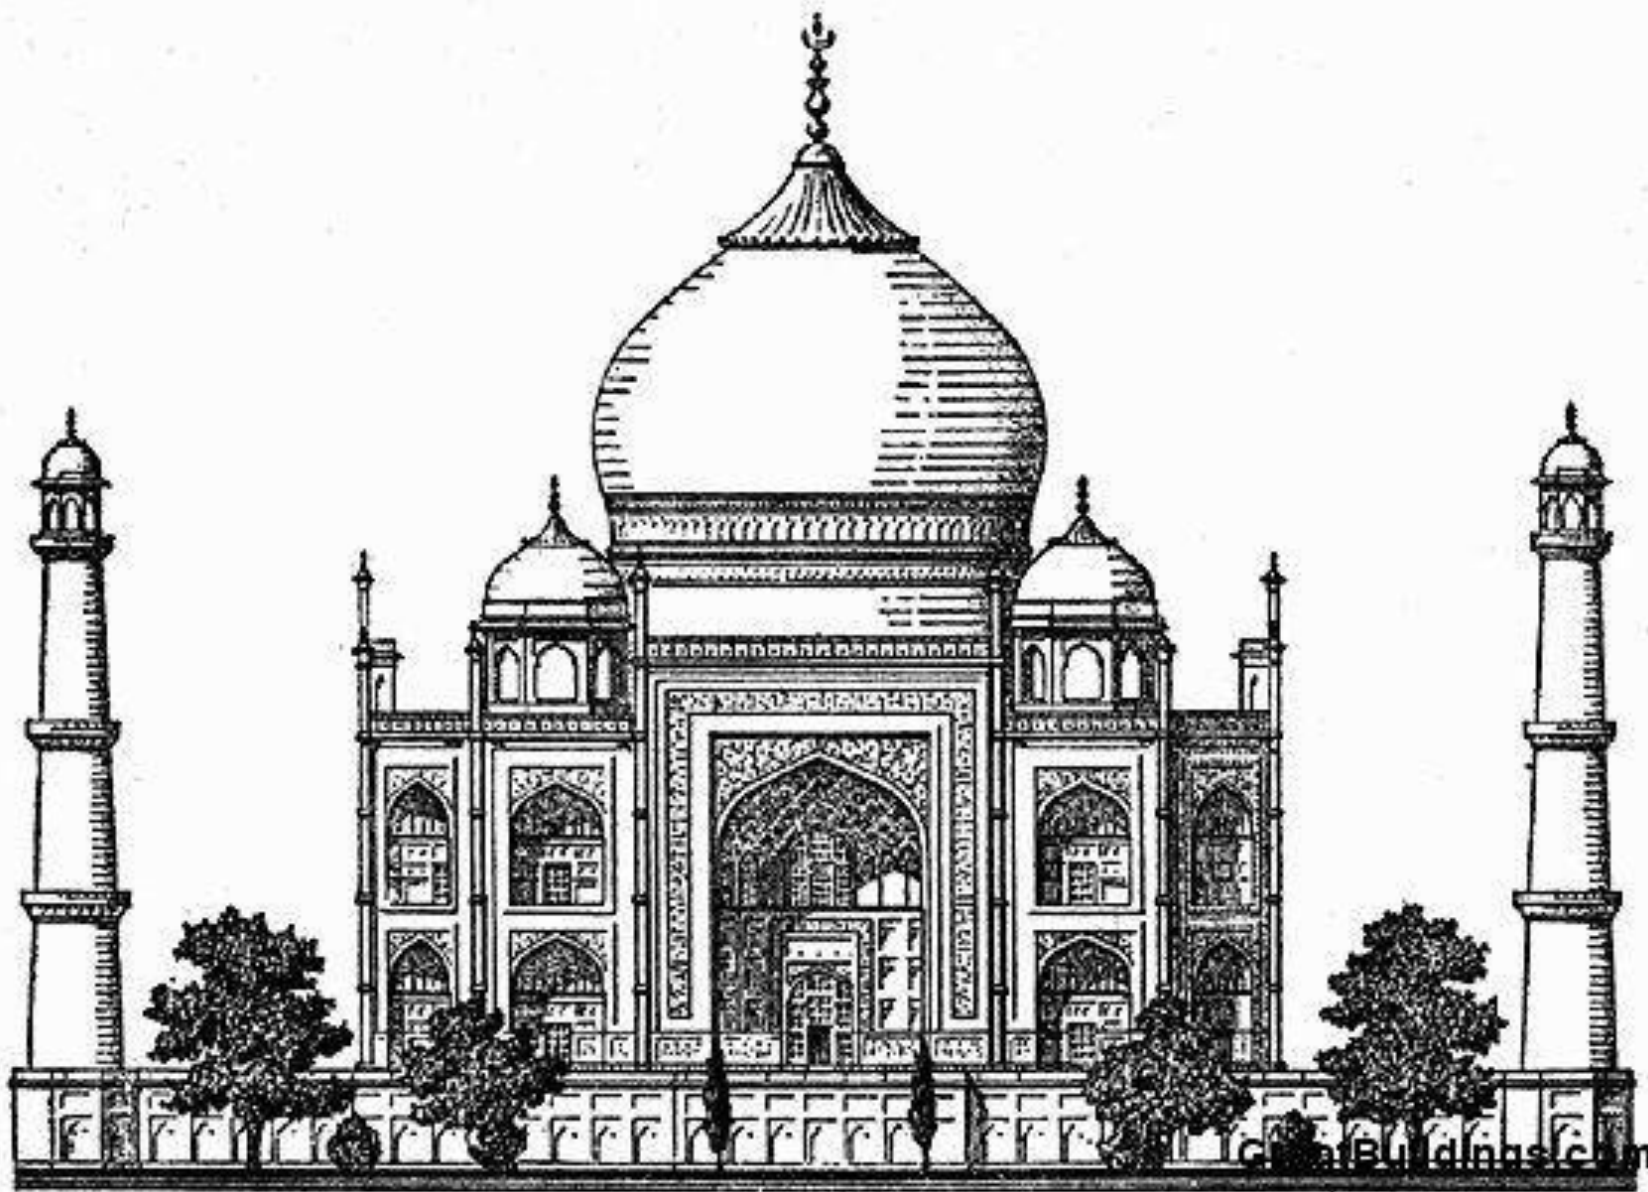


4. Plan Ottoman

Ce plan se trouve en Turquie (actuelle) principalement, et fut mis au point après la prise de Constantinople en 1453 par l'architecte Sinan. Il se compose d'une salle de prière sous une immense coupole cantonnée de demi-coupoles et de coupolettes. Souvent, les mosquées de type Ottoman font partie de grands complexes. On peut déceler une influence Byzantine (de **Sainte-Sophie** notamment).

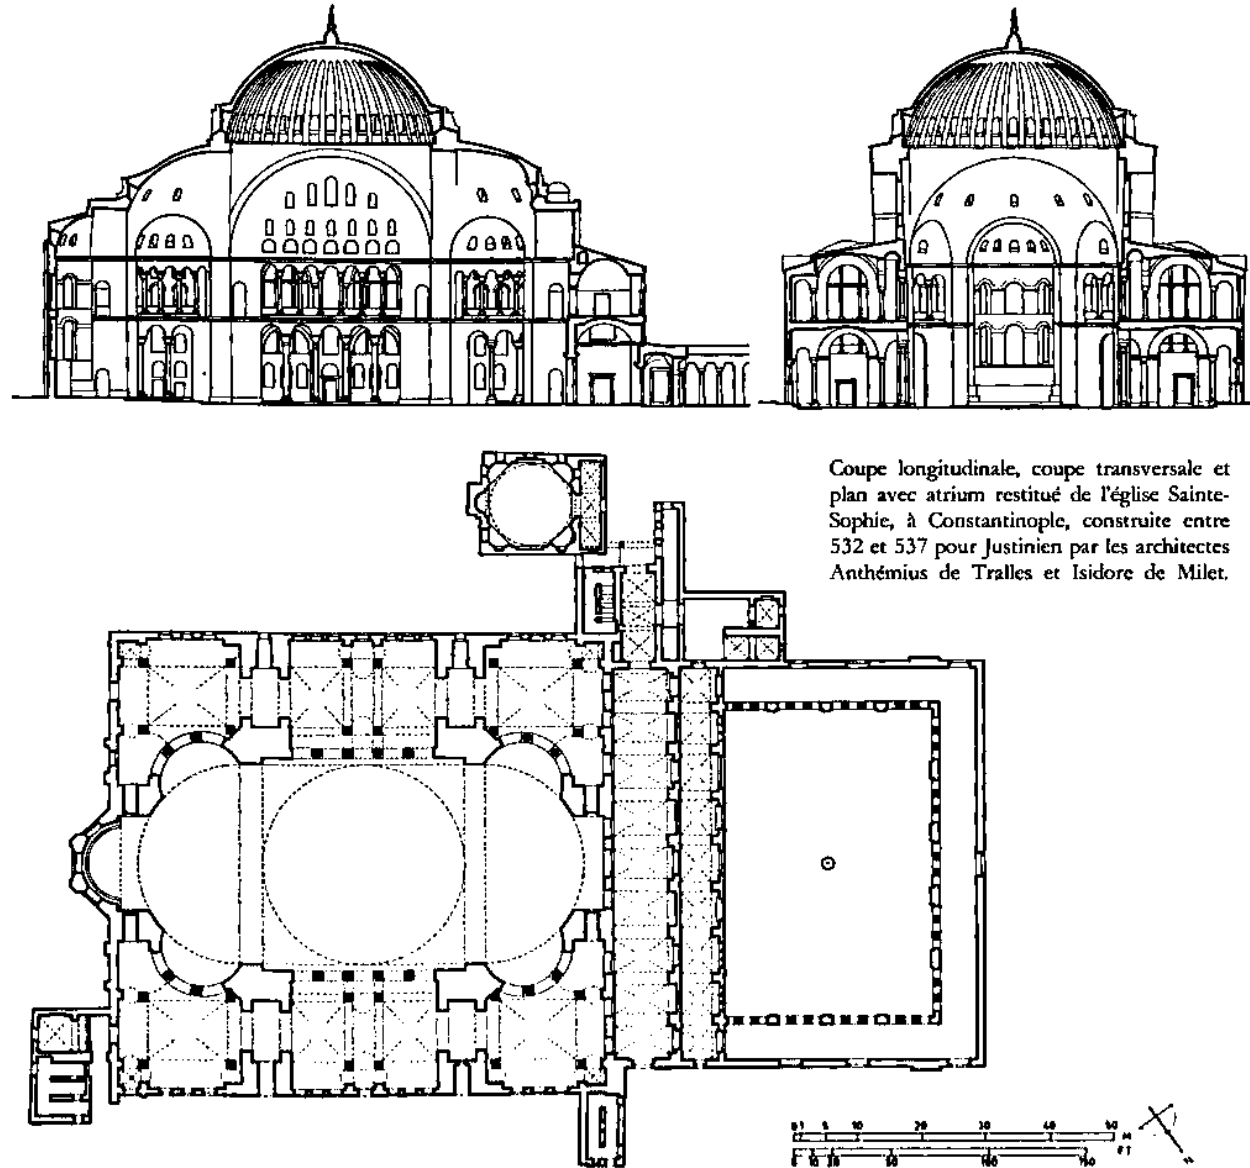

Coupe longitudinale, coupe transversale et plan avec atrium restitué de l'église Sainte-Sophie, à Constantinople, construite entre 532 et 537 pour Justinien par les architectes Anthémios de Tralles et Isidore de Milet.

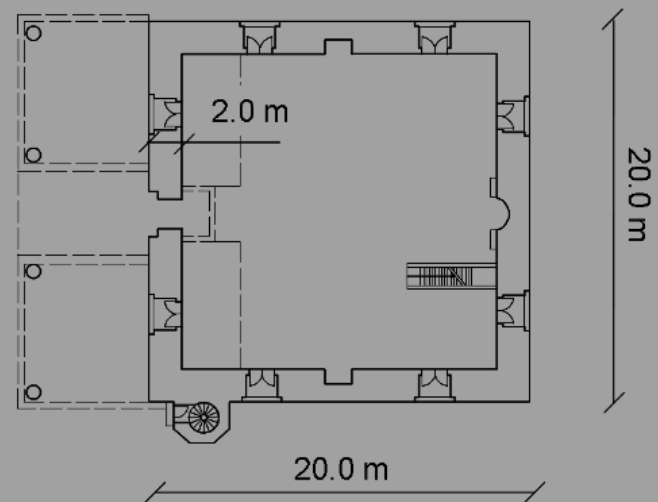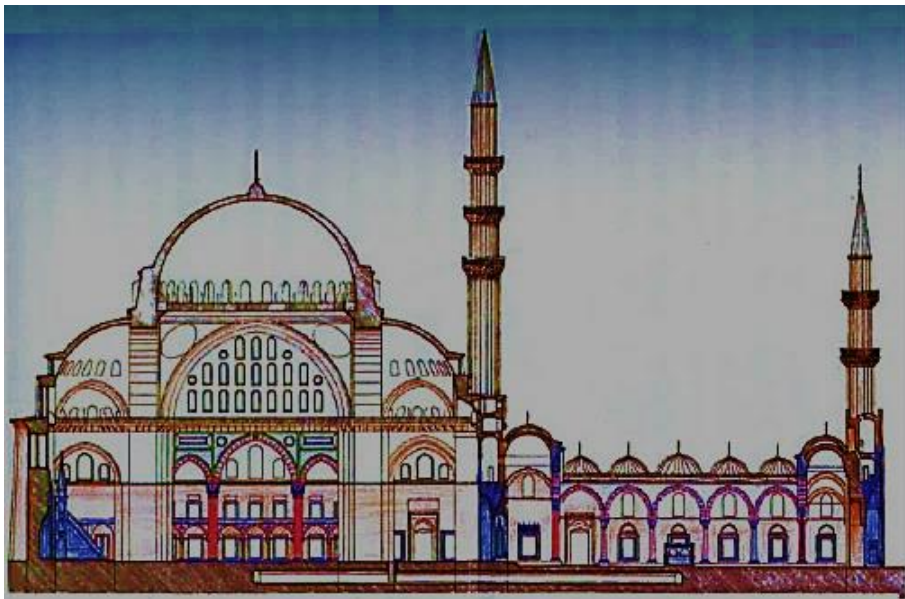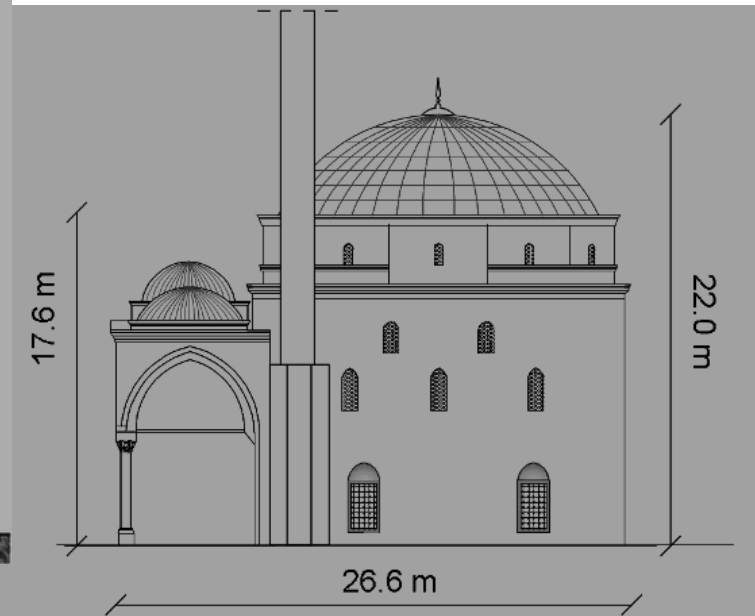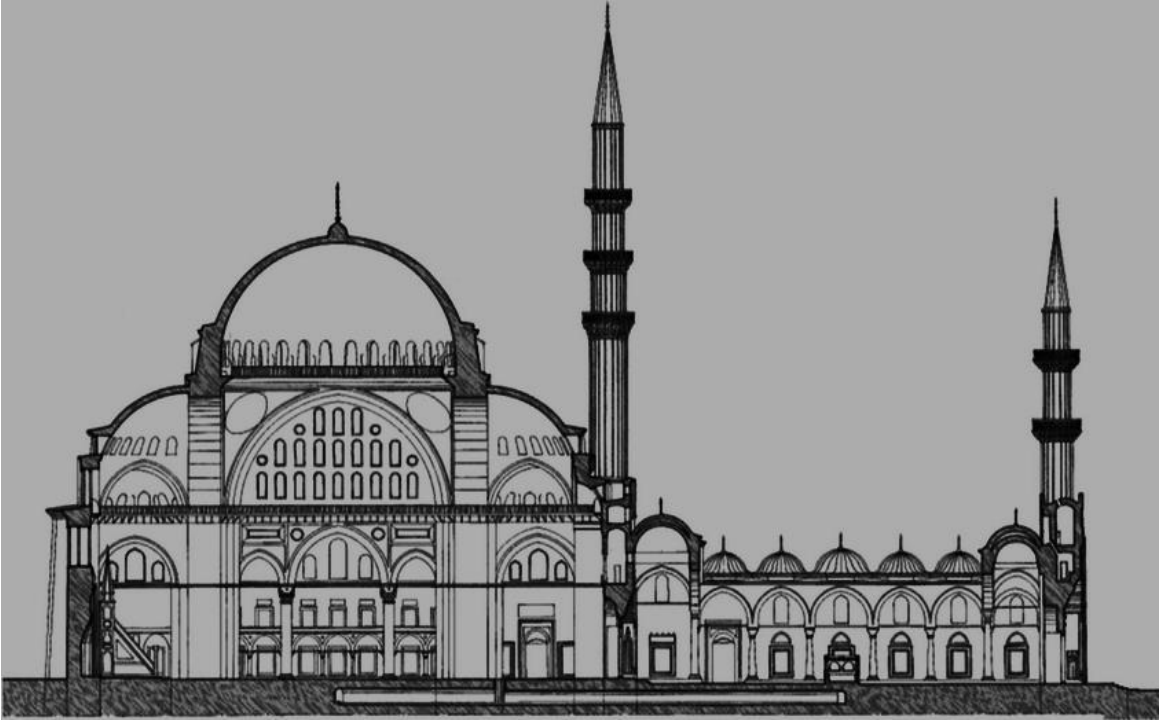


Archi is

Chapitre2 Partie 2. Mme Boudinar


2024

Mosquée El Suleimaniye

HORIZONTALSCHNITT DURCH DEN TAMBÜR DER HAUPTKUPPEL

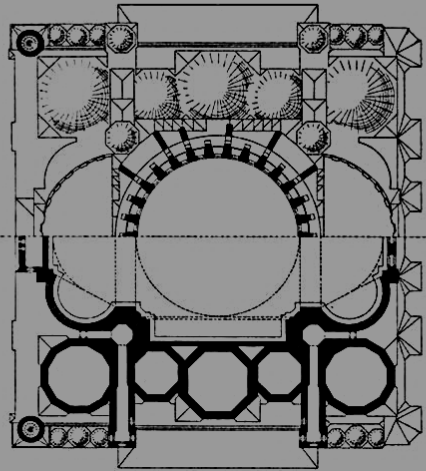


HORIZONTALSCHNITT DURCH DIE TAMBÜRE
DER KLEINEN KUPPELN

 


19,n MOSCHEE DES SULTAN SULEIMAN I.
(SULTAN SULEIMAN DSCHAMI)

SEITENANSICHT

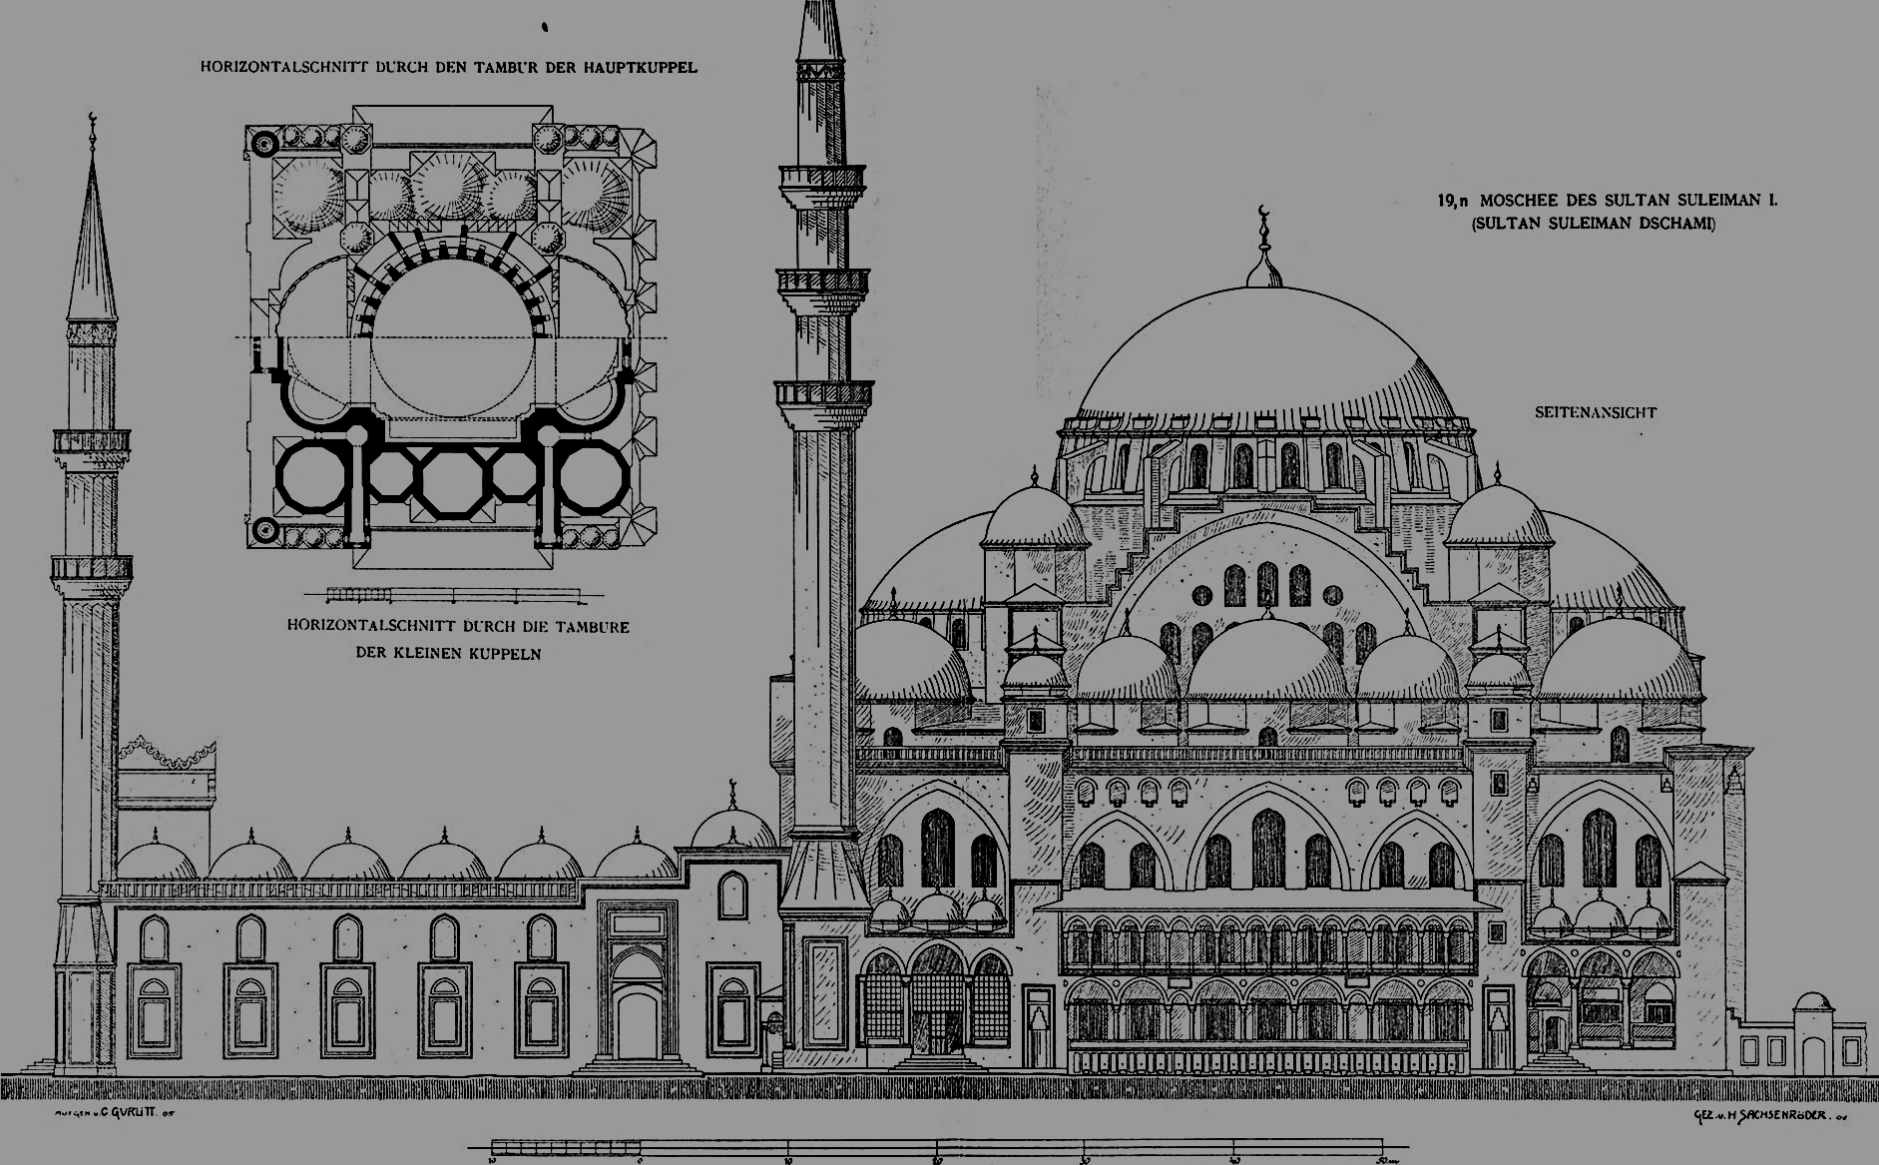



LÄNGSSCHNITT


GRUNDRISSE

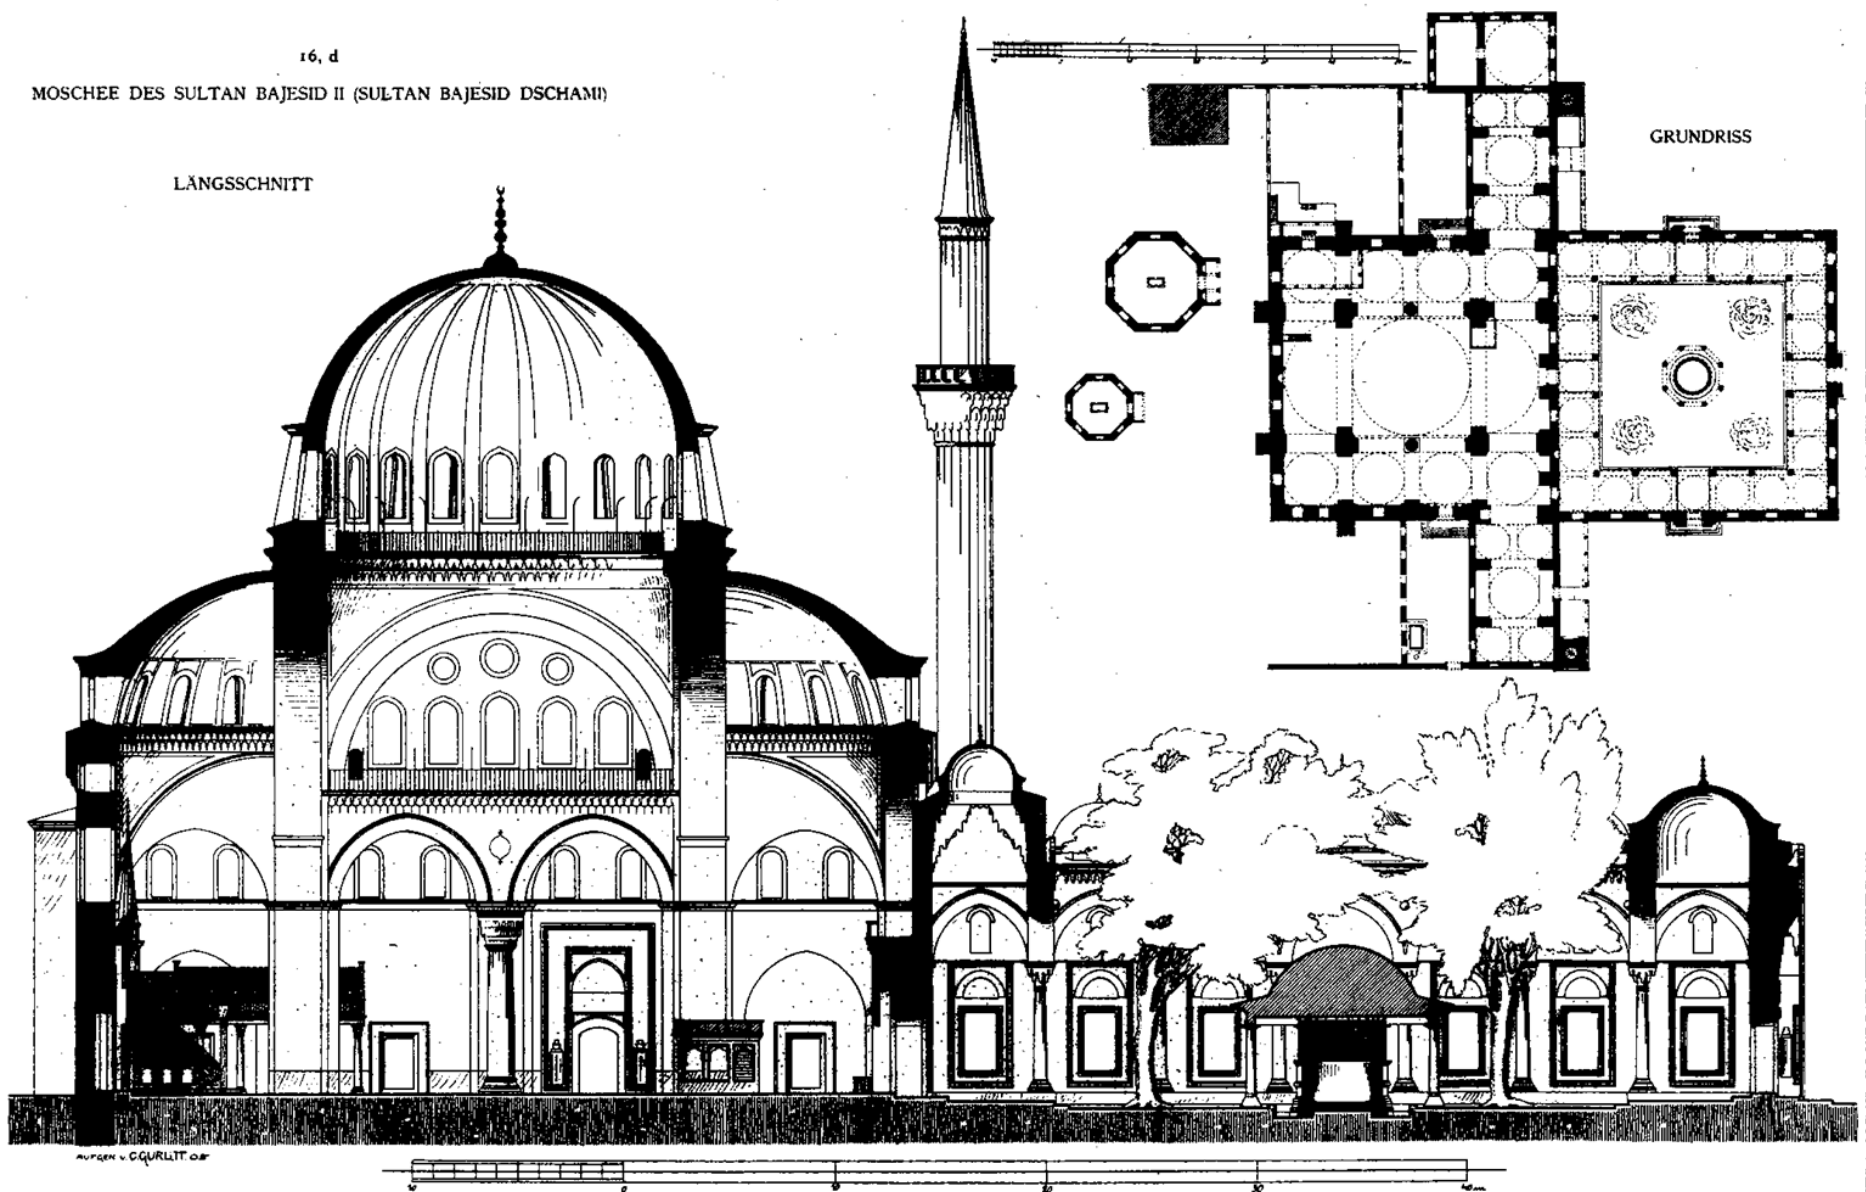



Mosquée Bayezid II

Mosquée Bali Pasha

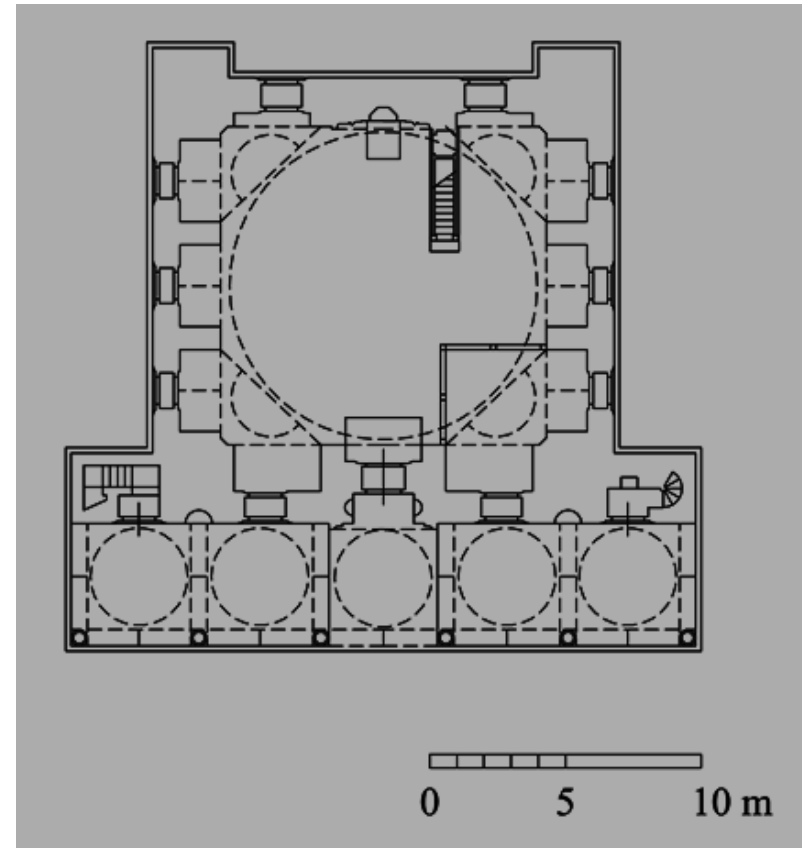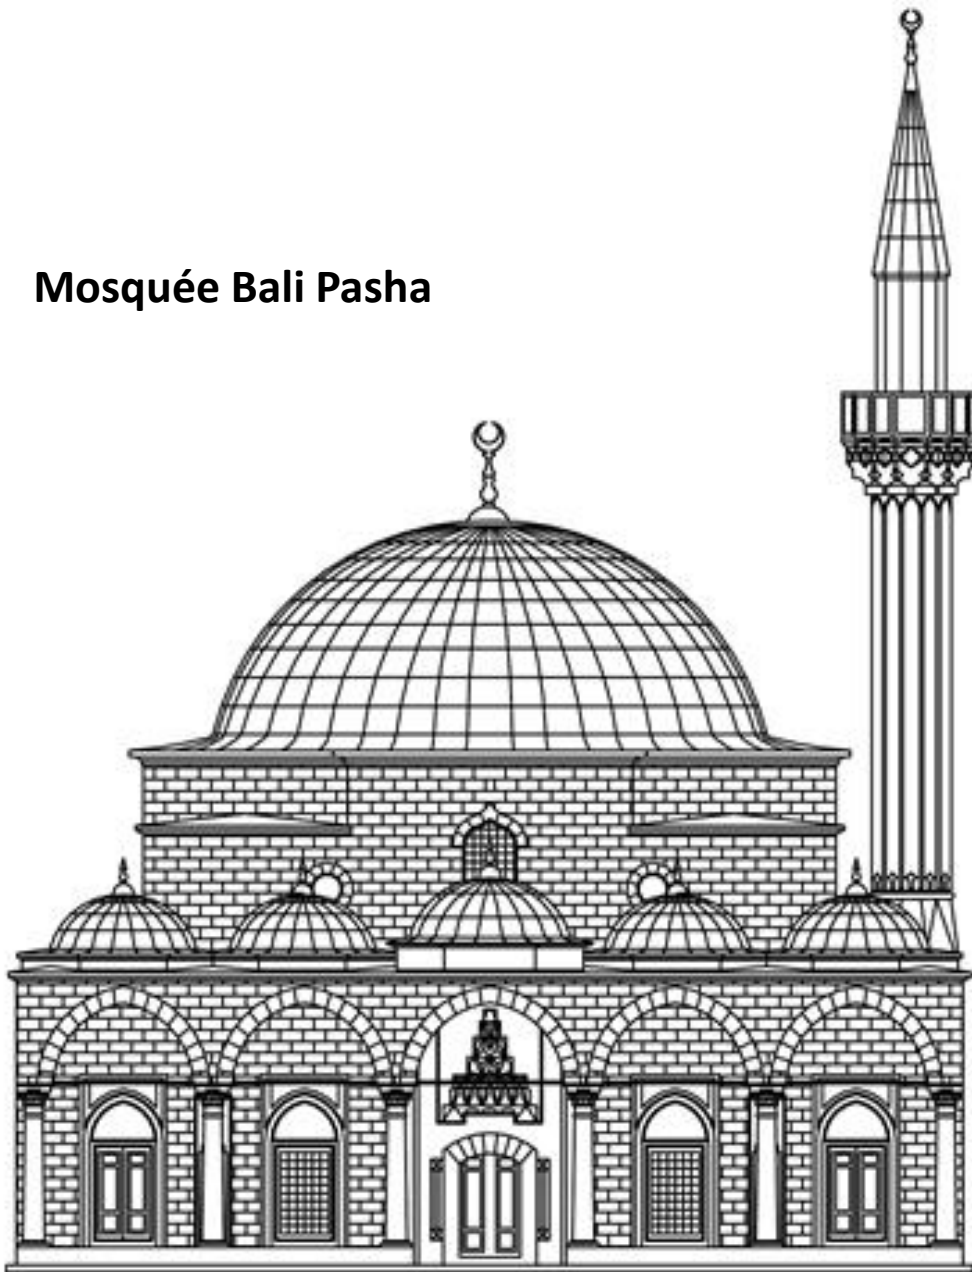

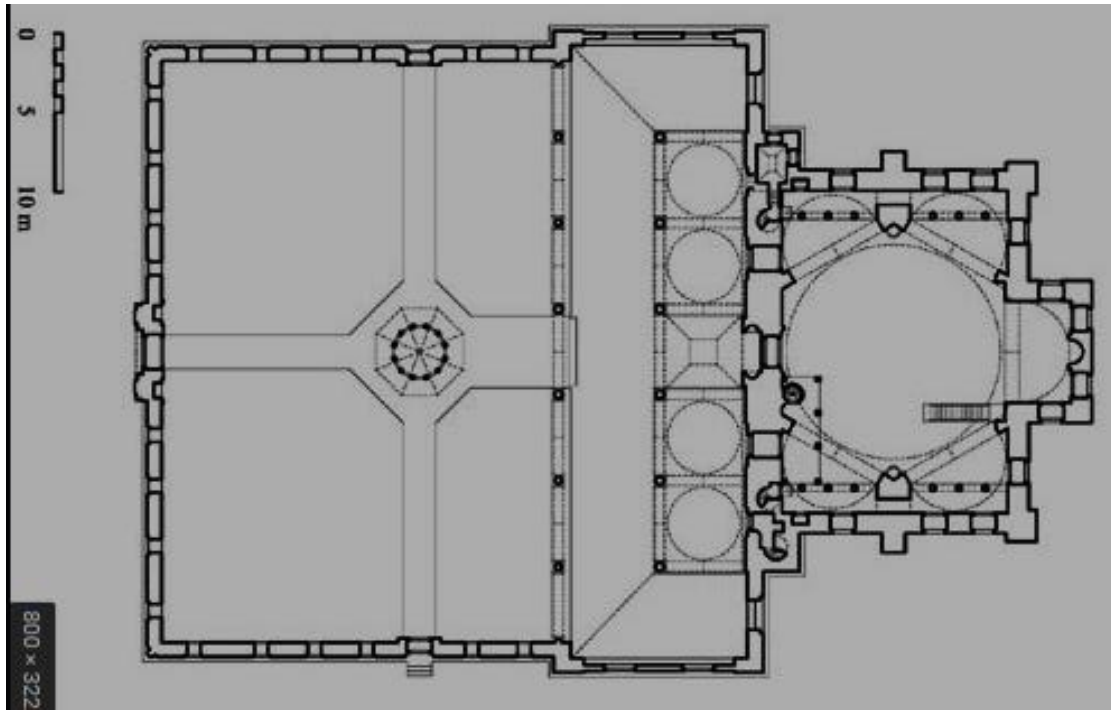

Mosquée Semiz Ali Pasha

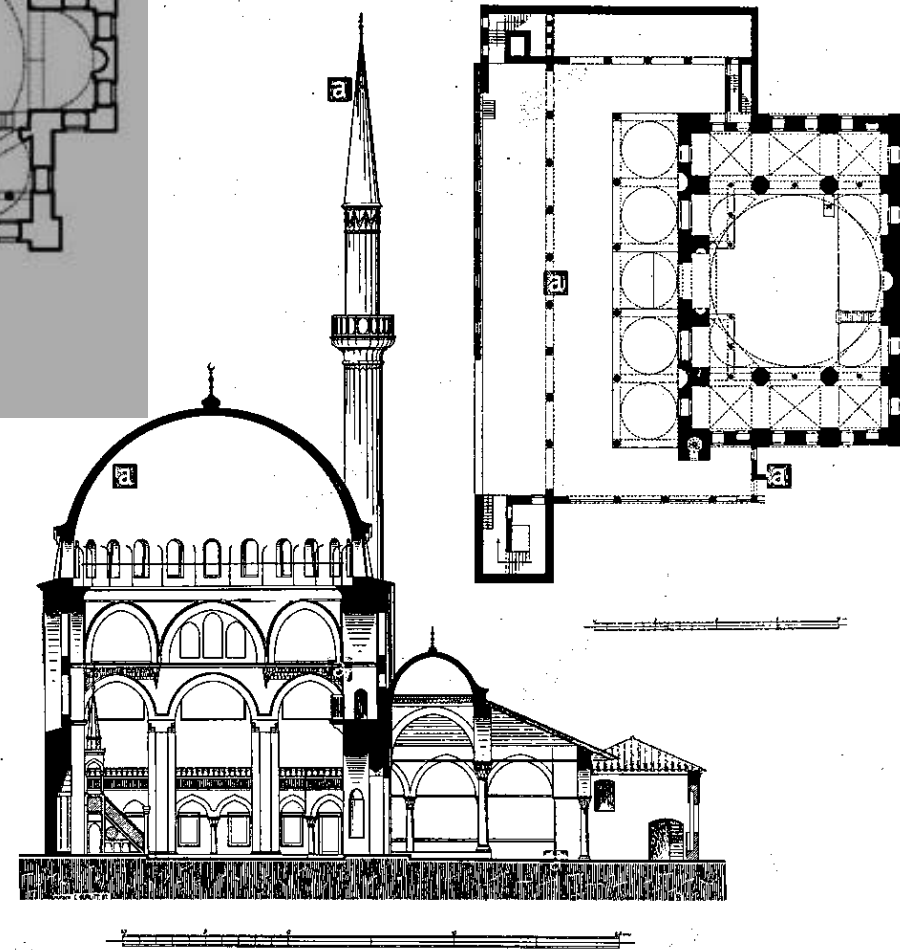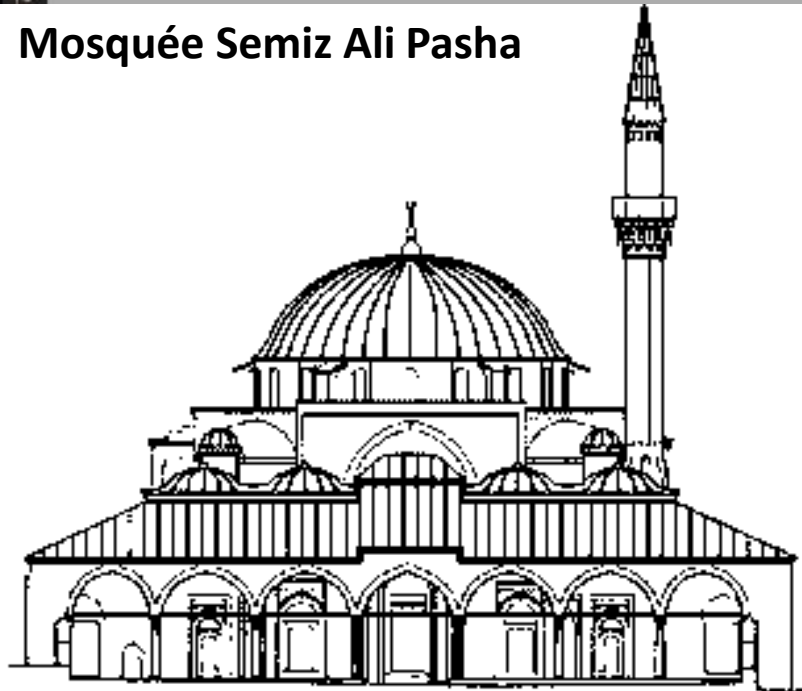

Mosquée Rustum Pacha

